




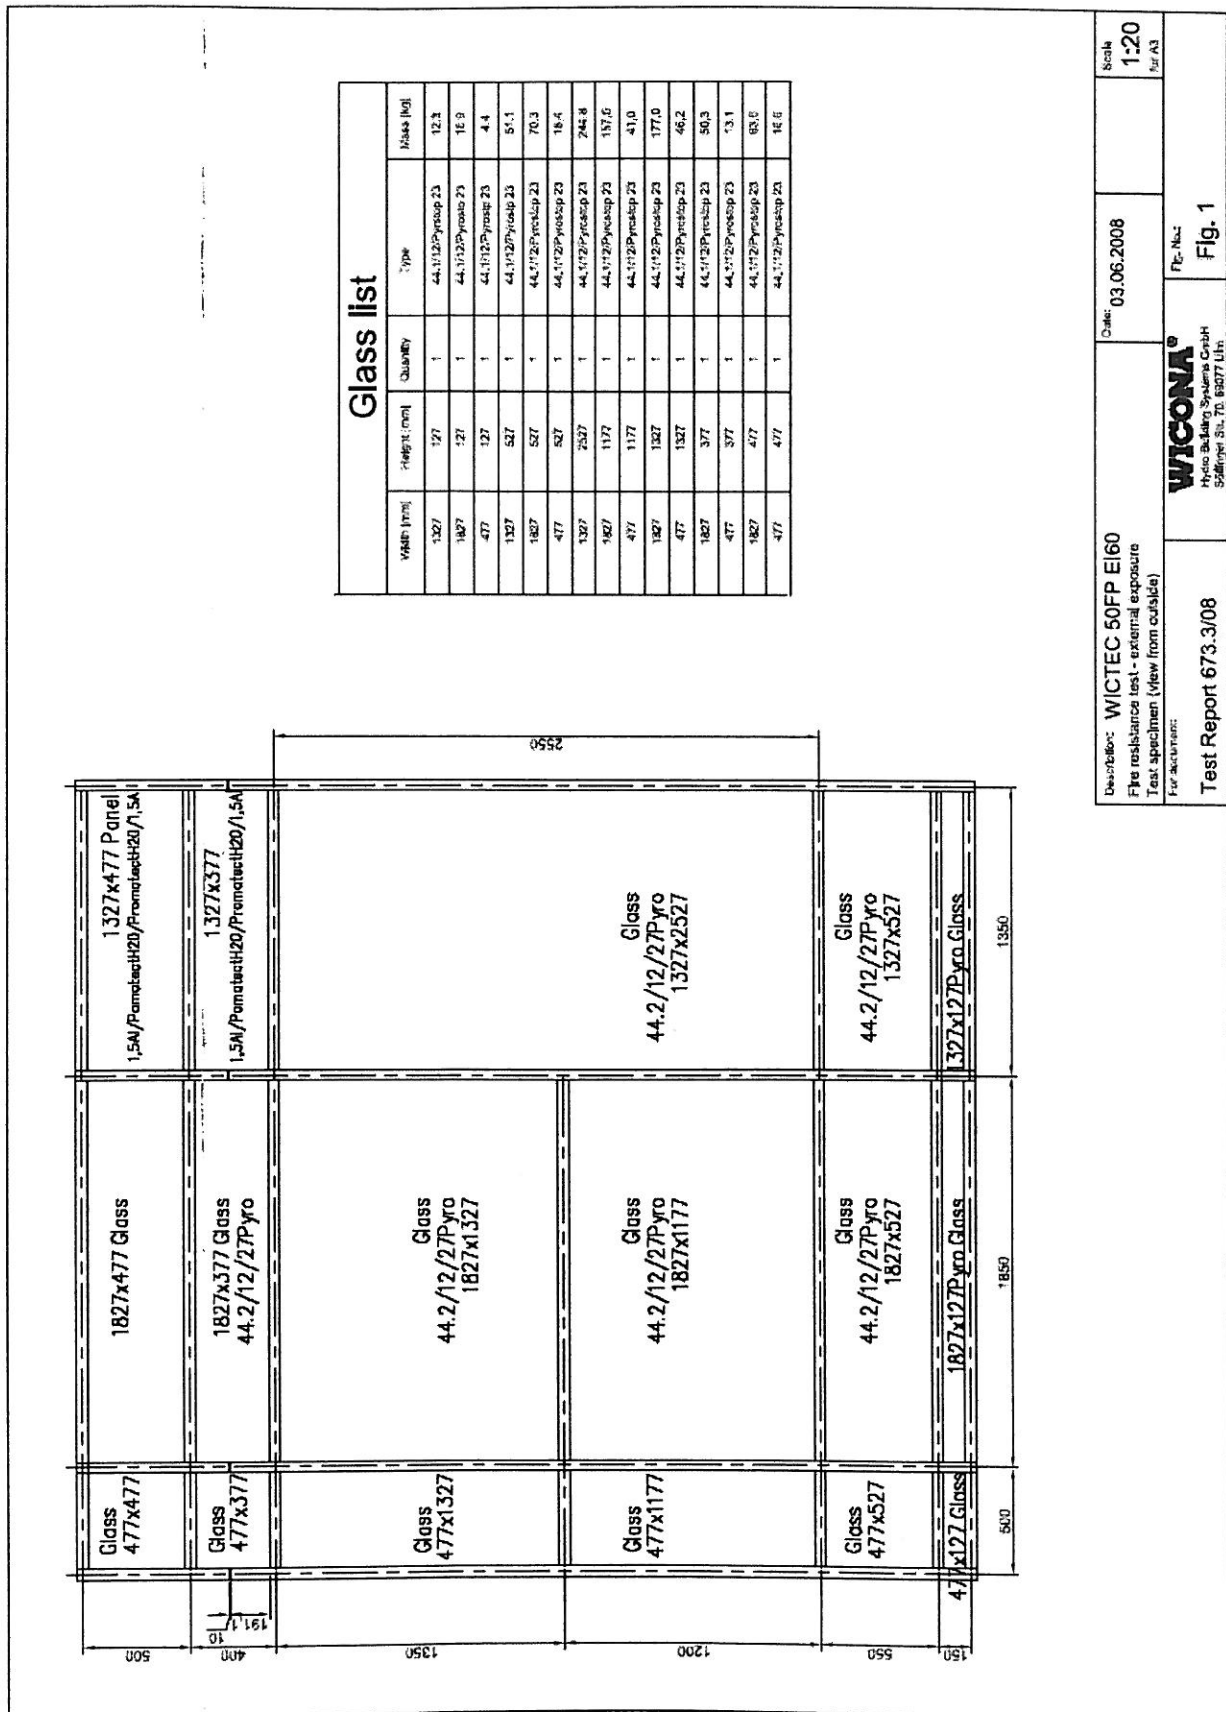


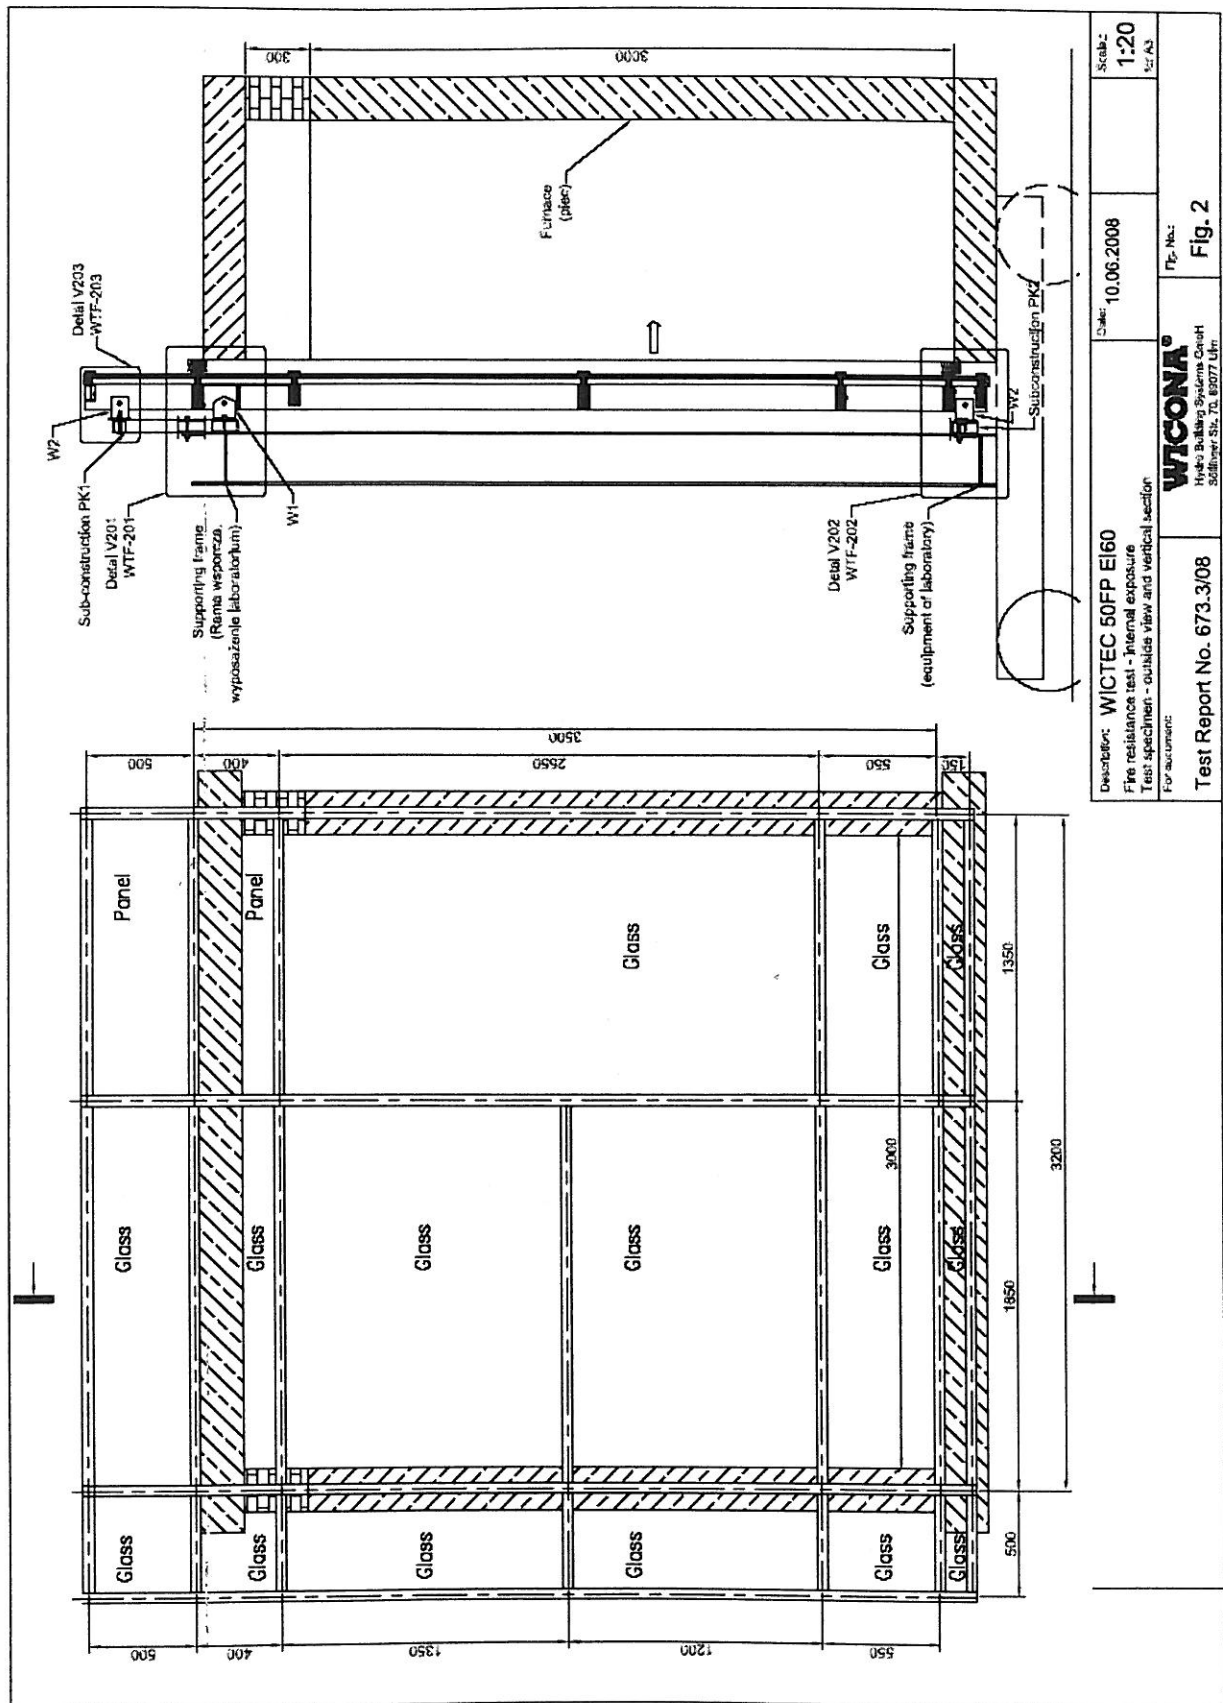

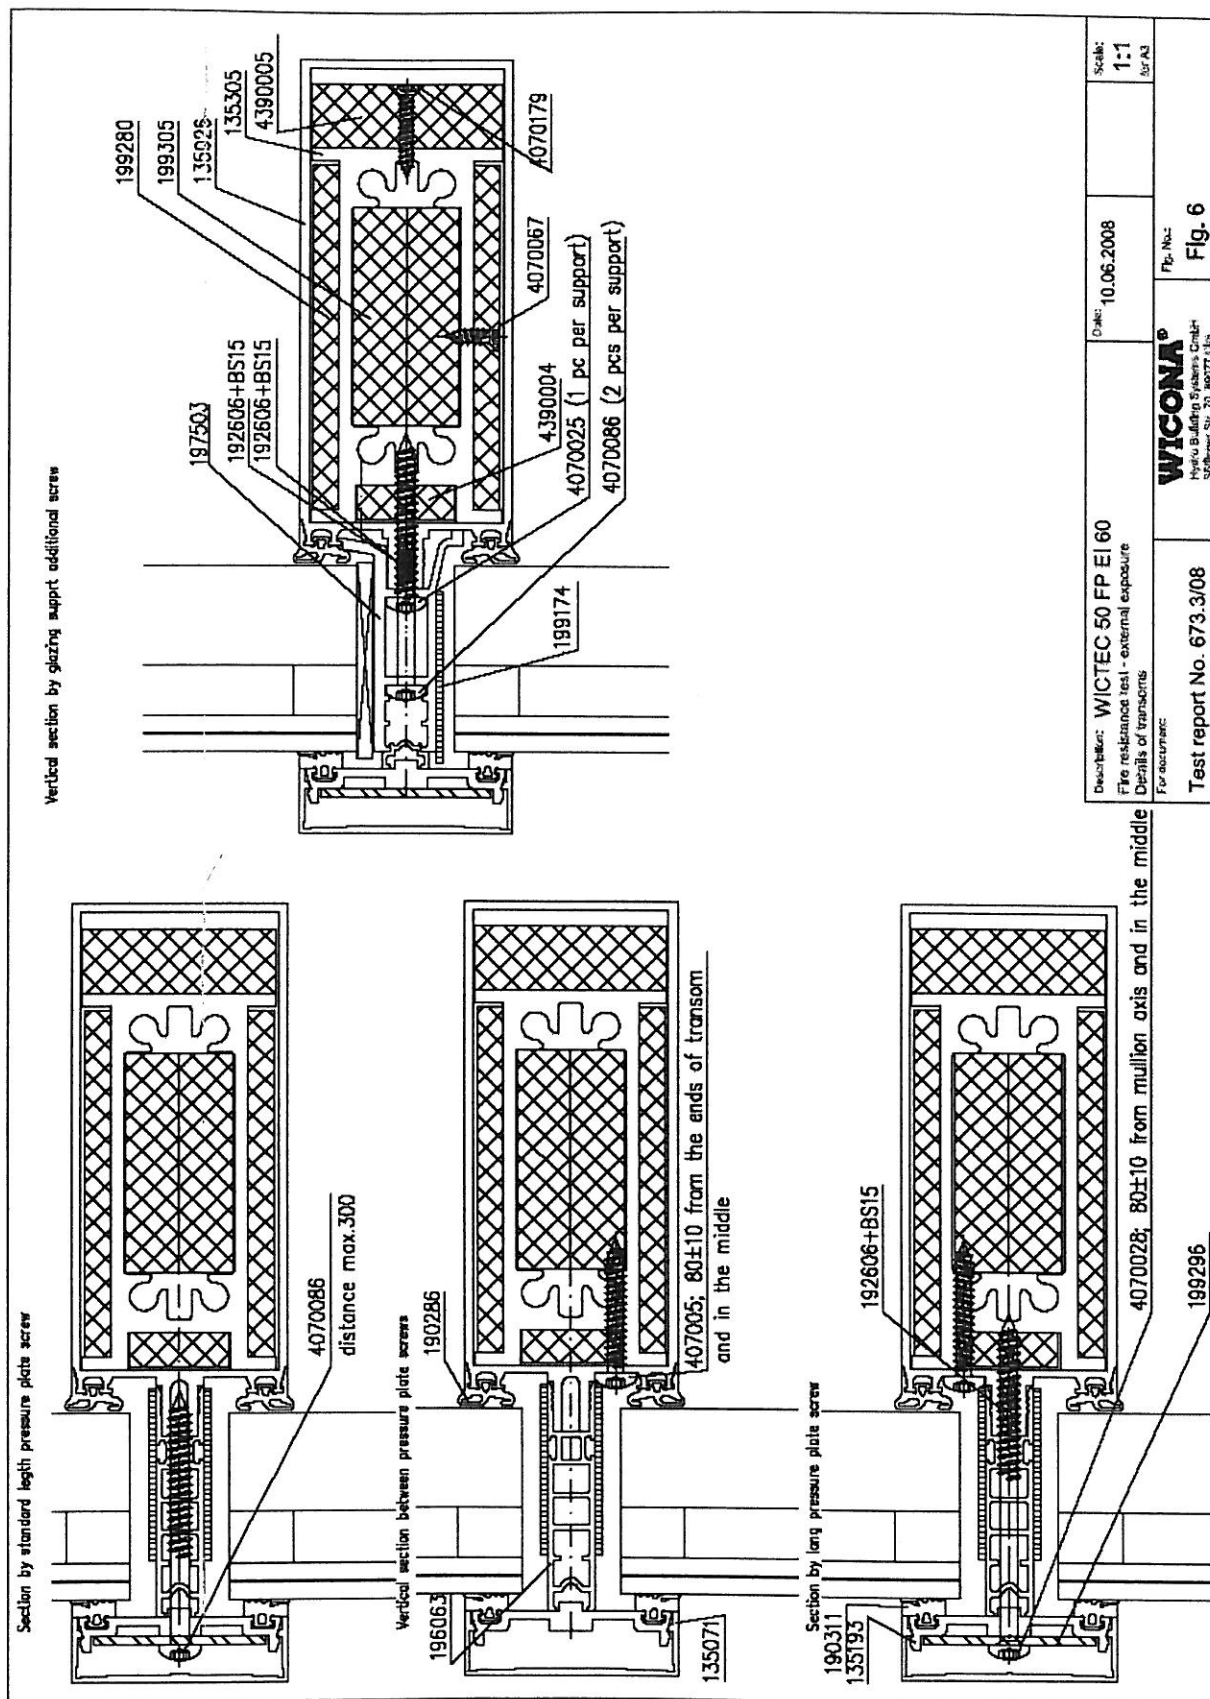


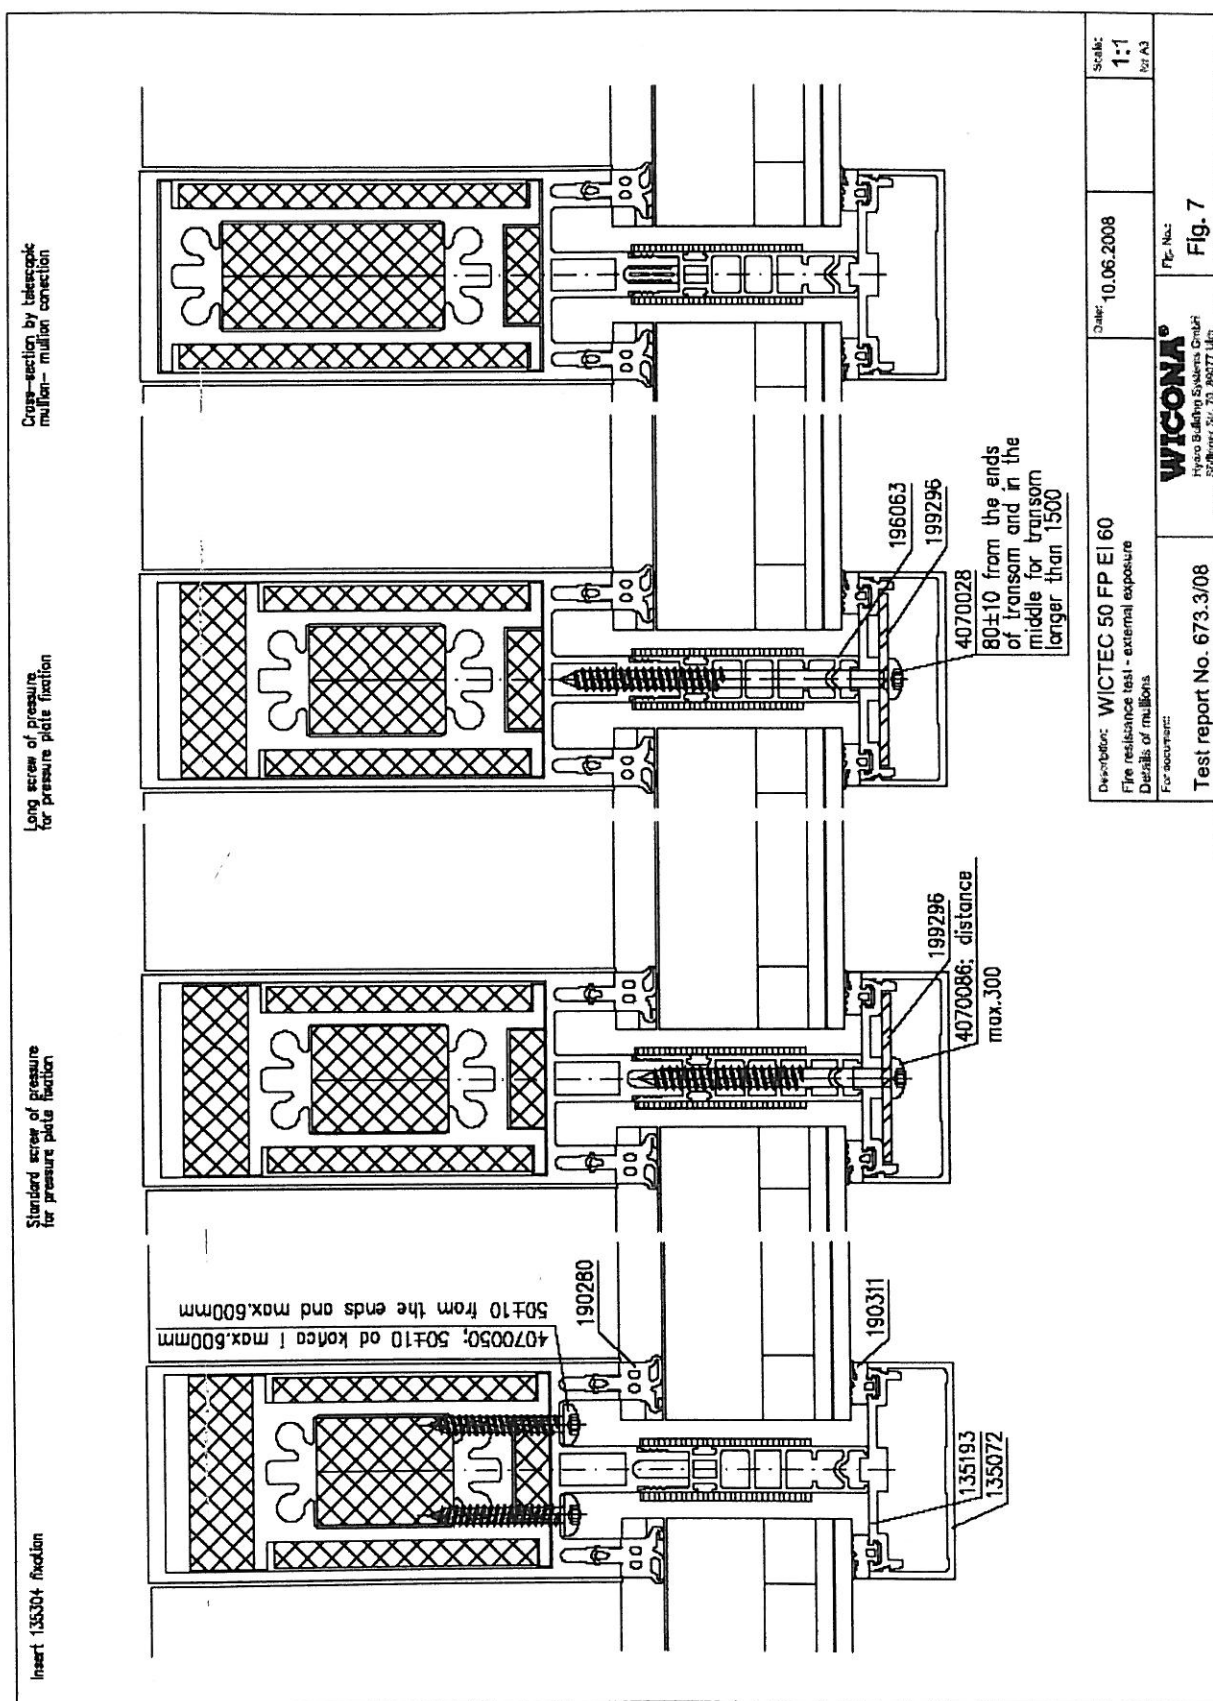

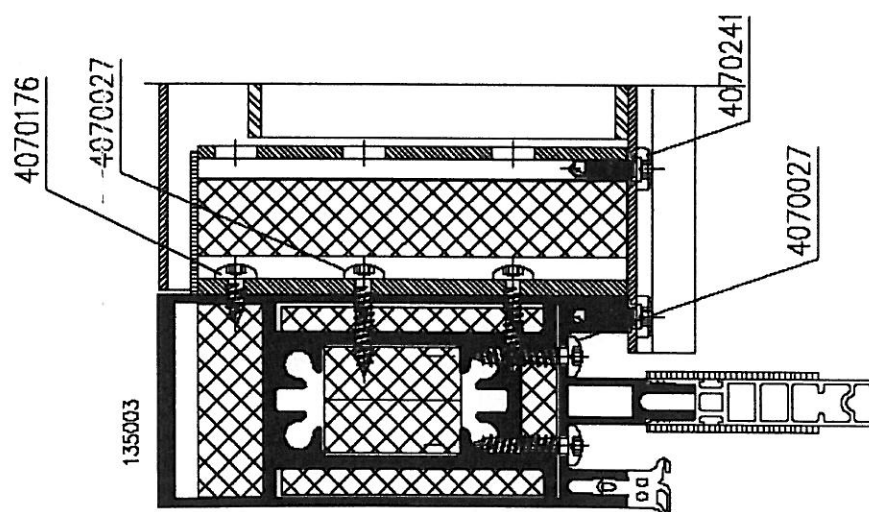


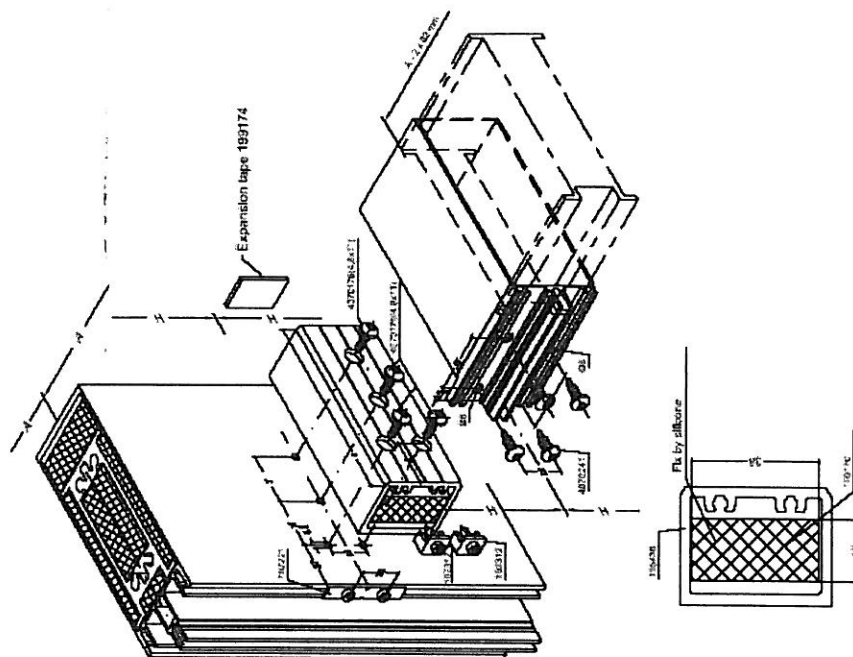

Description: WICTEC 50 FP EI 60 Fire resistance test - external exposure Detail of transom - mullion connection For document:	Date: 10.06.2008	Scale: 1:1 for A3
Test report No. 673.3/08	Fig. No.: Fig. 8	WICONA® Hydro Building Systems GmbH Schiller Str. 70, 89077 Ulm

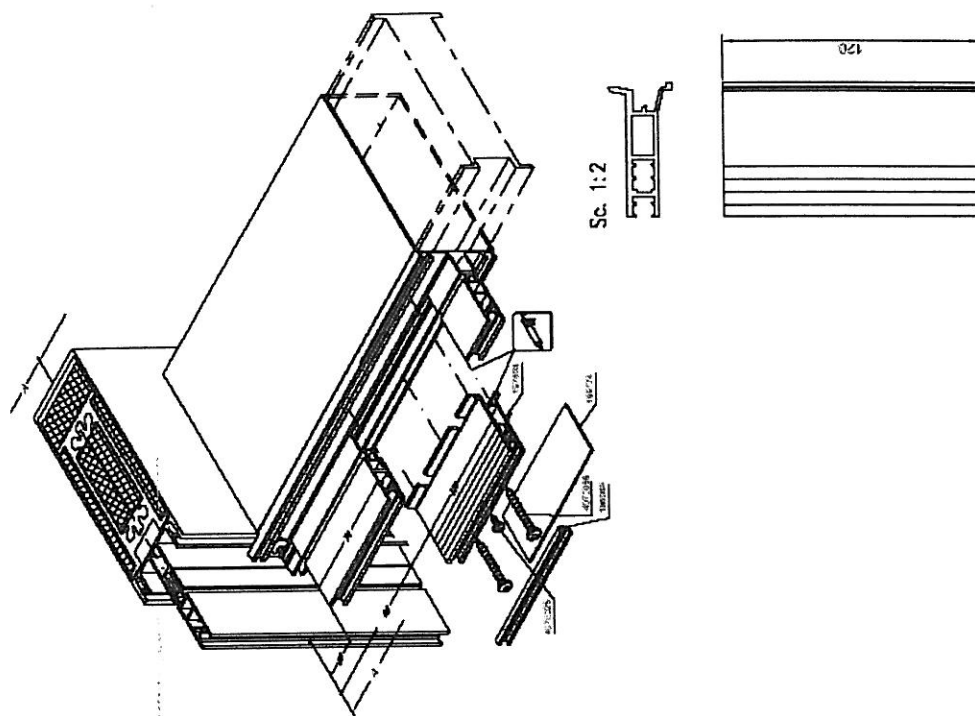

Sc. 1:2

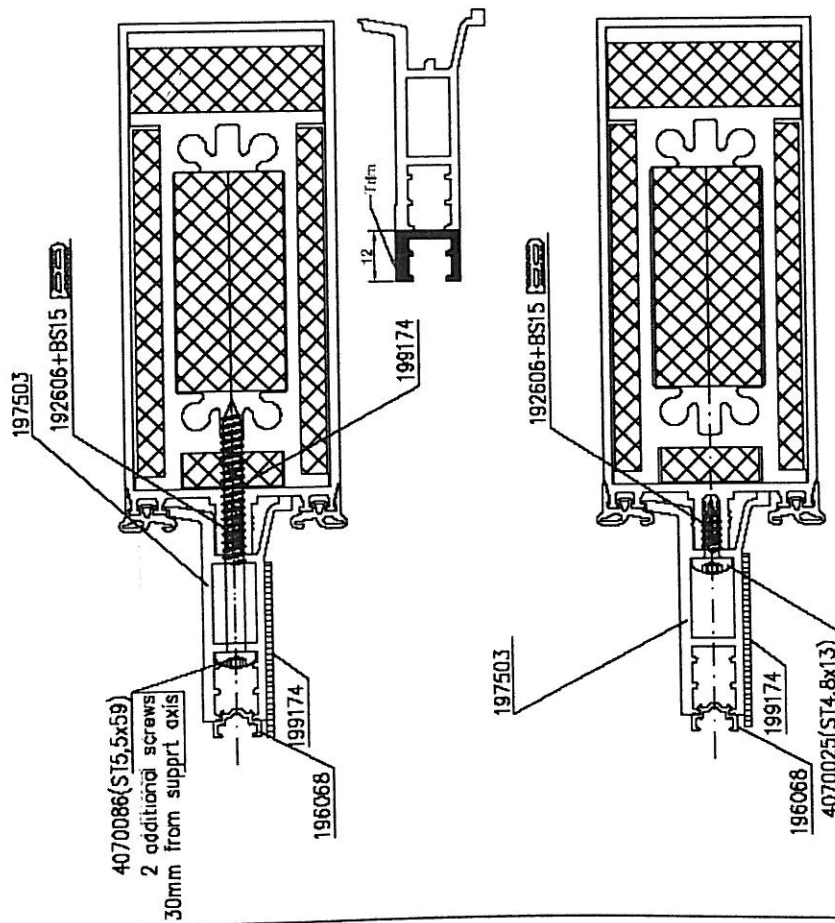

Description:	WICTEC 50 FP EI 60	Date:	10.06.2008
File resistance test - external exposure	Details of glass supporting	Scale:	1:1
For document:	WICONA®	Fig. No.:	Fig. 9
Test report No. 673.3/08	Hydra Building Systems GmbH	Sollinger Str. 10, 49577 Ulfen	

